


Gebäudeschnitt und Nordansicht

Wohnhof Am Steinbogen 18 | Hildesheim | Acht Wohnungen zur Vermietung

1 Schnitt Süd nach Nord

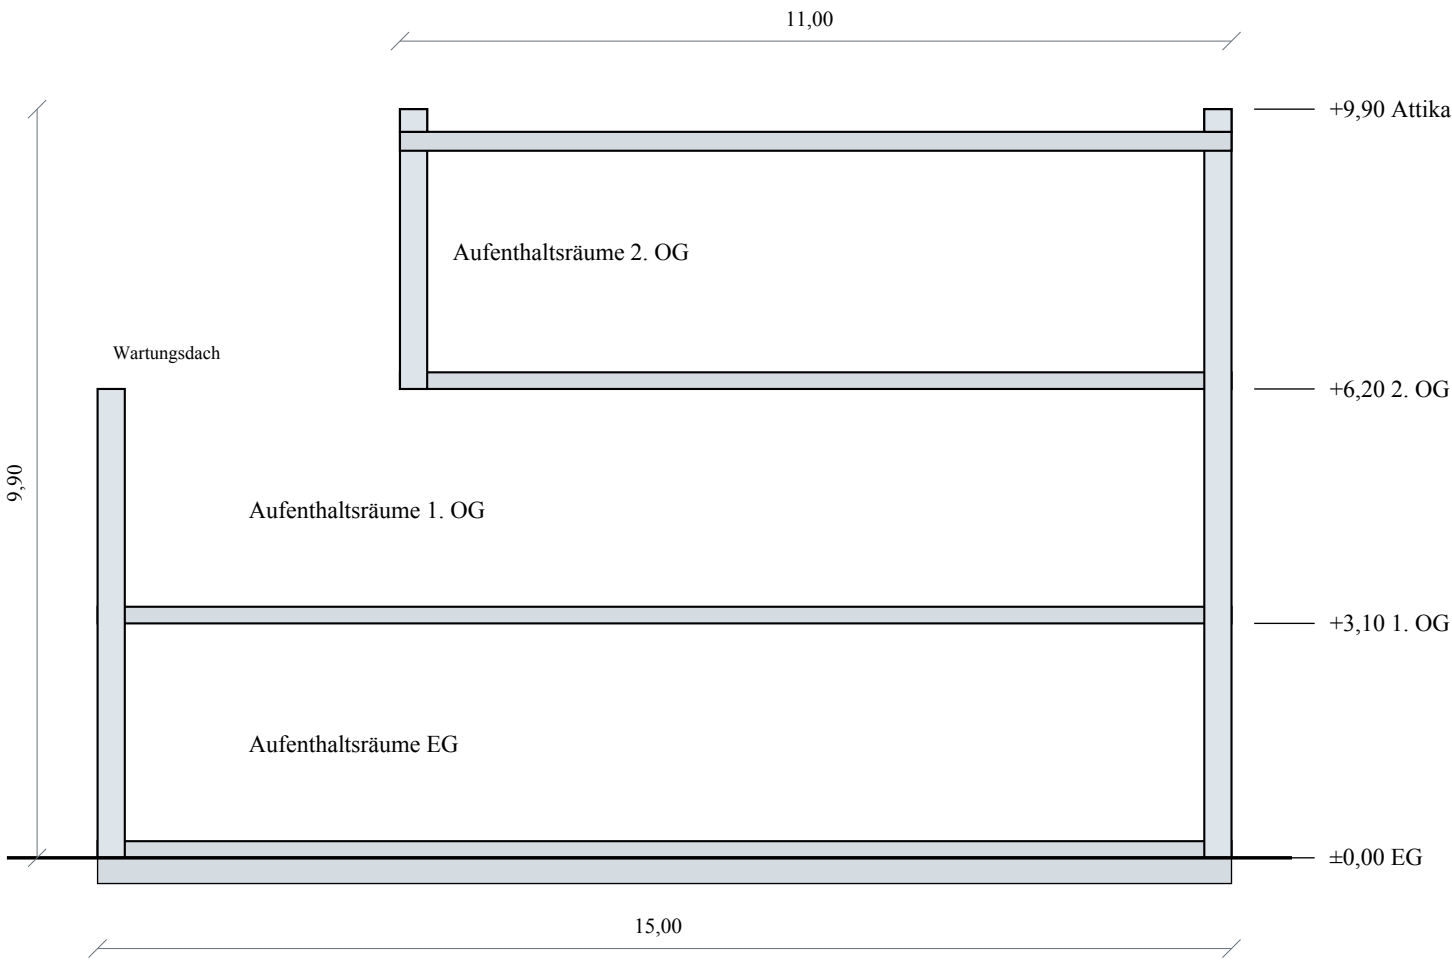

3 Bezug und Gebäudehöhe

Bezugsgelände ±0,00 an der Nordfassade.

Höchster Aufenthaltsraumfußboden +6,20.

Drei Vollgeschosse, kein Keller.

Schnittdarstellung 1 zu 100.

4 Planungsstand

Deckenstärke als Arbeitsansatz 22 cm.

Endgültige Statik gesondert.

Dachaufbau nach Wärmeschutzplanung.

Dachoberfläche oben +9,60 m.

Unterkante Bodenplatte -0,34 m.

BRI 220 x 9,94 + 80 x 6,54

= 2.710,00 m³; ohne Attikaufschlag.

2 Nordansicht 1 zu 160

