


Ausführungsdetails Eingang und Sanitärschacht

Wohnhof Am Steinbogen 18 | Hildesheim | Acht Wohnungen zur Vermietung


1 Eingangsschwelle AP02 1 zu 10

Ausführungsstand 21.08.2027 | Freigabe Objektplanung und Fachplanerkoordination
Maße vor Ort prüfen. Produktbezogene Werkplanung bleibt vor Bestellung abzugleichen.

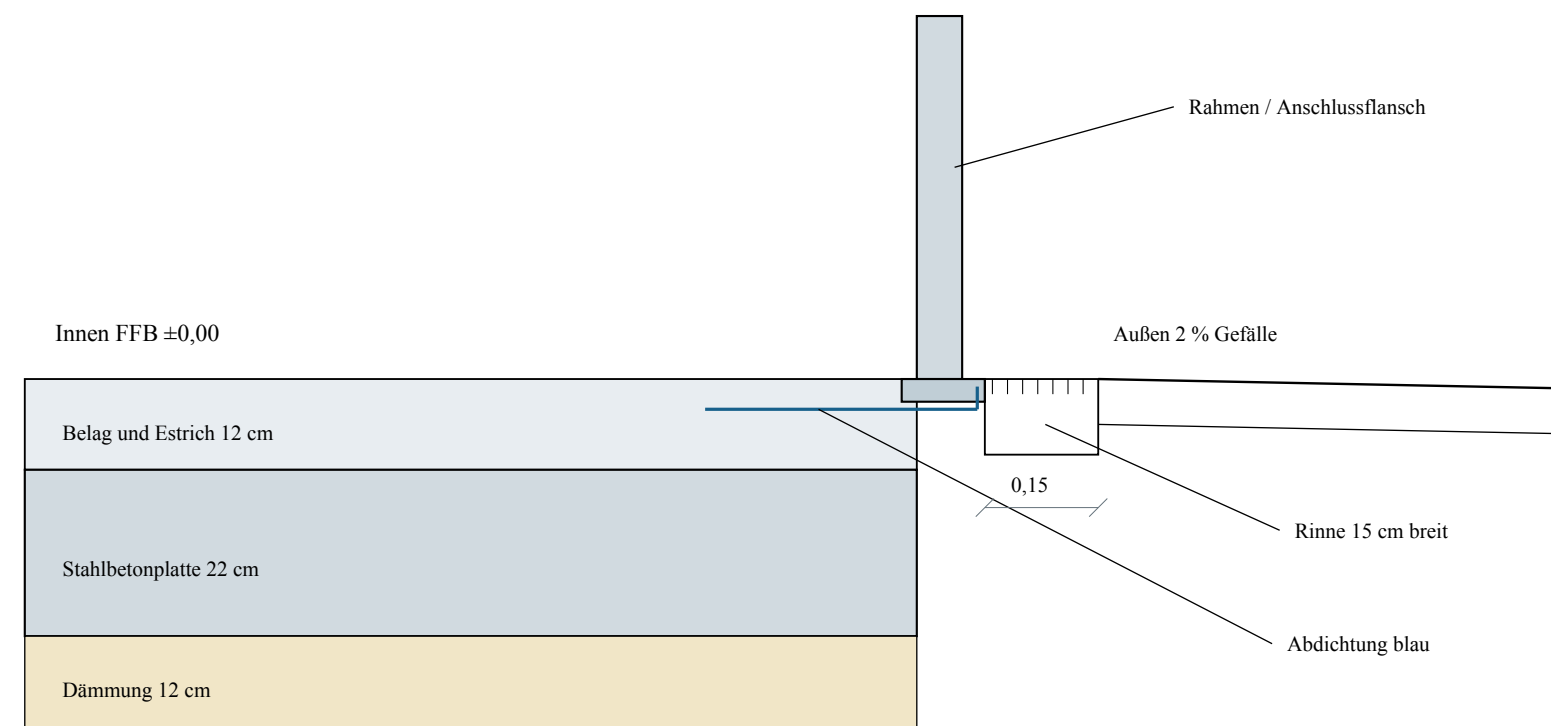

- Schwelle ohne Höhenversatz; Türöffnung lichte Breite 0,90 m.
- Entwässerungsrinne unmittelbar vor dem Rahmen, an Entwässerung anschließen.
- Abdichtung mit geeignetem Anschlussflansch durchgehend anschließen.
- Die Türfirma und Abdichtungsfirma stimmen das konkrete System vor Fertigung ab.
- Keine nachträgliche Schwellenaufkantung ohne neue Freigabe.

2 Deckenöffnung AP03 1 zu 10

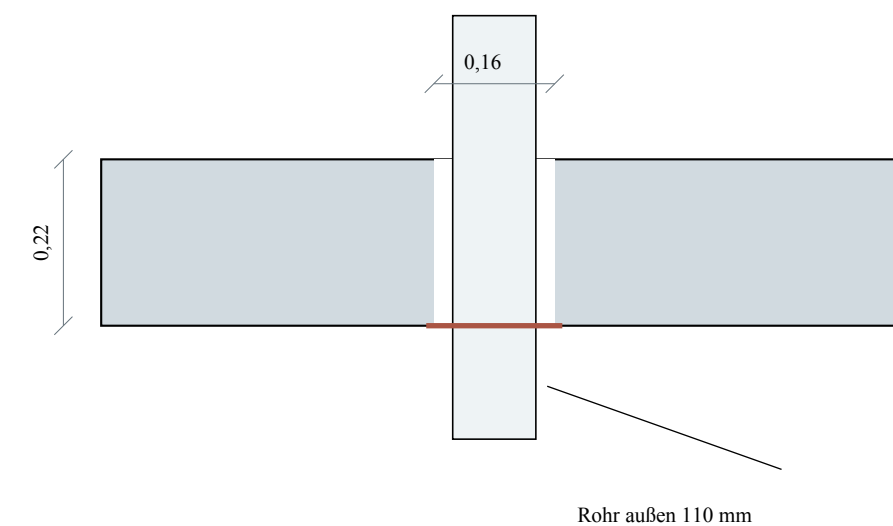

- Öffnung 160 x 160 mm im Sanitärschacht.
- Lage nach freigegebener Aussparungsliste.
- Keine zusätzliche Bohrung im Auflagerbereich.
- Abschottung passend zu Bauteil und Rohrsystem.
- Eignung und Einbau nach Systemnachweis.
- Ausführung vor Verschluss fotografisch erfassen.
- Keine Vergrößerung ohne Tragwerksfreigabe.