


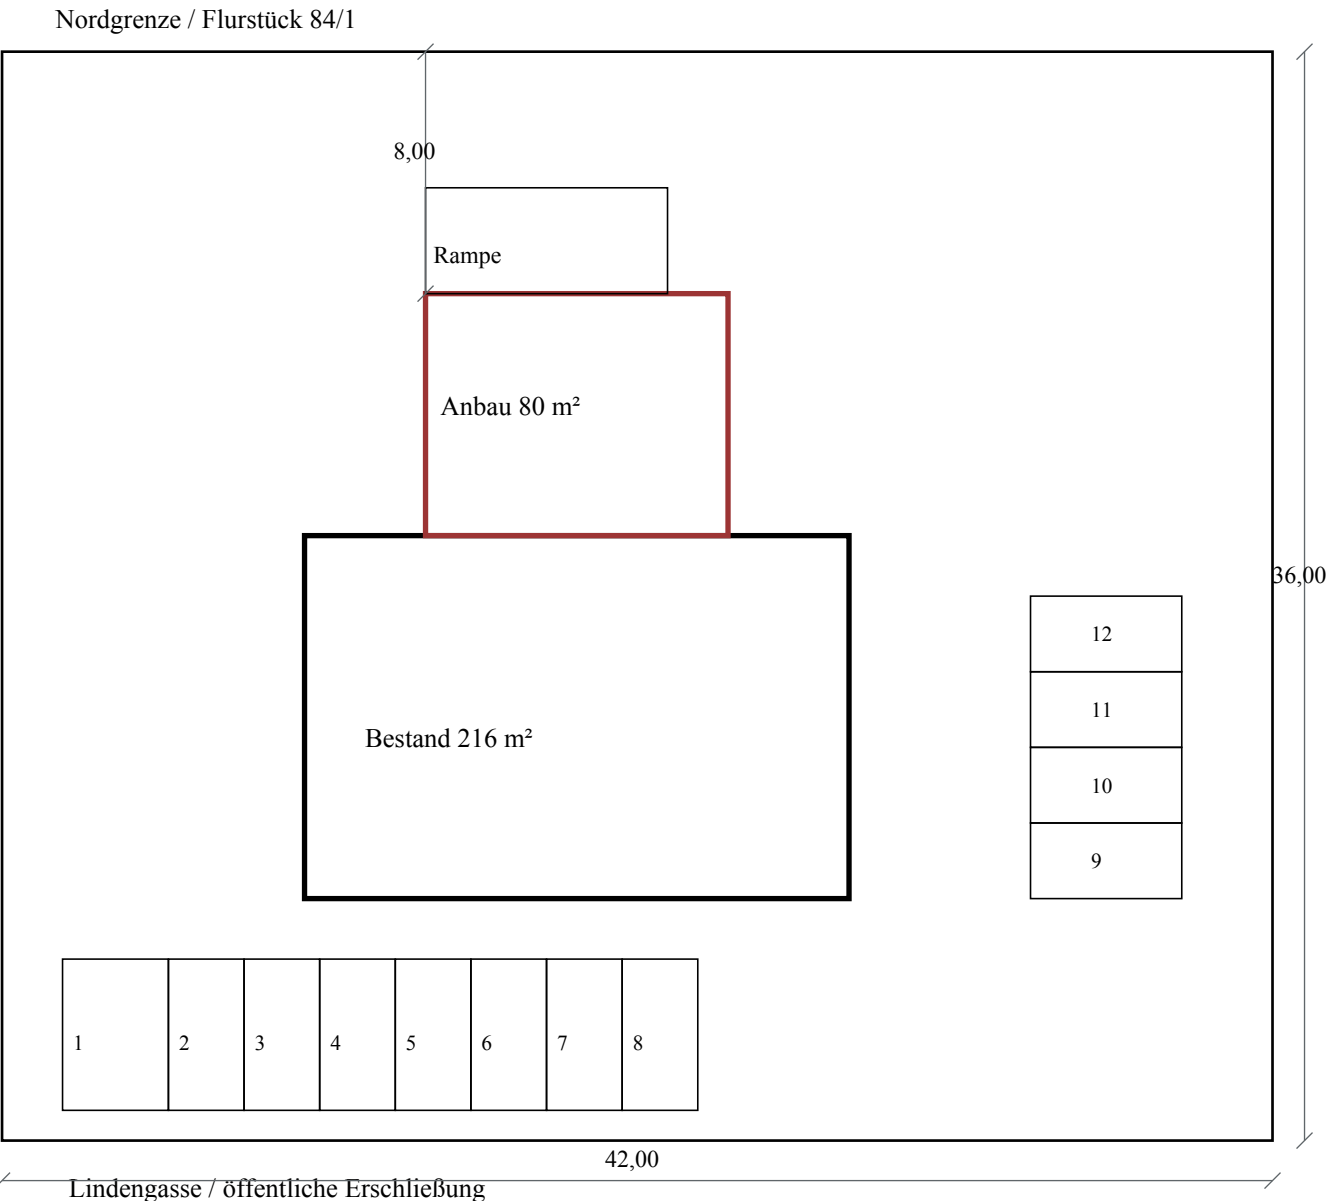

Flur 14 · Flurstück 83/7

- Grundstück: 1.512 m²
- Maßstab 1:250 bei A4
- Westnachbar: 83/6
- Ostnachbar: 83/8
- Zwölf Kfz-Stellplätze
- Acht Fahrradplätze westlich
- Regenwasseranschluss: Nordhof
- Keine Inanspruchnahme fremden Grunds

1 Erläuterungen und Zeichnungsangaben

Bauherr: Bürgerhaus Leinewinkel e.V., Lindengasse 18, 37574 Einbeck. Entwurfsverfasserin: Lena Hartwig, Mühlenweg 7, 37574 Einbeck. Baugrundstück: Gemarkung Einbeck, Flur 14, Flurstück 83/7, Fläche 1.512 m². Das Blatt ist der objektbezogene Lageplan der Entwurfsverfasserin nach den vom Bauherrn übergebenen Grundstücksangaben; es wird kein amtliches Vermessungssiegel geführt.

Grundstück 42,00 m breit und 36,00 m tief. Der Bestand liegt 10,00 m von der Westgrenze und 8,00 m von der Straßengrenze entfernt. Seine Grundfläche beträgt 216 m². Der Anbau liegt 14,00 m von der Westgrenze entfernt und endet 8,00 m vor der Nordgrenze. Seine Grundfläche beträgt 80 m². Überbaute Fläche gesamt 296 m², Verhältnis zur Grundstücksfläche rund 0,196.

Der Abstand des Bestands zur Ostgrenze beträgt 14,00 m. Das Grundstück wird von Süden über die Lindengasse erschlossen. Zwölf Kfz-Stellplätze liegen südlich und östlich des Gebäudes; Stellplatz 1 ist auf 3,50 m verbreitert. Acht Fahrradplätze liegen westlich des Rampenzugangs. Der Zugang zu beiden Ausgängen bleibt auf dem eigenen Grundstück.

Nachbarflächen sind westlich Flurstück 83/6, nördlich 84/1 und östlich 83/8. Es ist keine Bebauung auf fremdem Grund beantragt. Die eingezeichnete Regenwasserleitung folgt dem geplanten Anschluss an den vorhandenen Grundstücksstrang; die endgültige Höhenlage wird vor Ausführung ermittelt. Grundlage der Beurteilung ist der Bauantrag vom 20.01.2022 mit Baubeschreibung B-01.

Empfänger: Stadt Einbeck · Bauaufsicht. Bezug: Bauvorhaben Lindengasse 18. Anlagen: keine. Zeichnung und Erläuterungsblatt bilden einen gemeinsamen Planstand.