


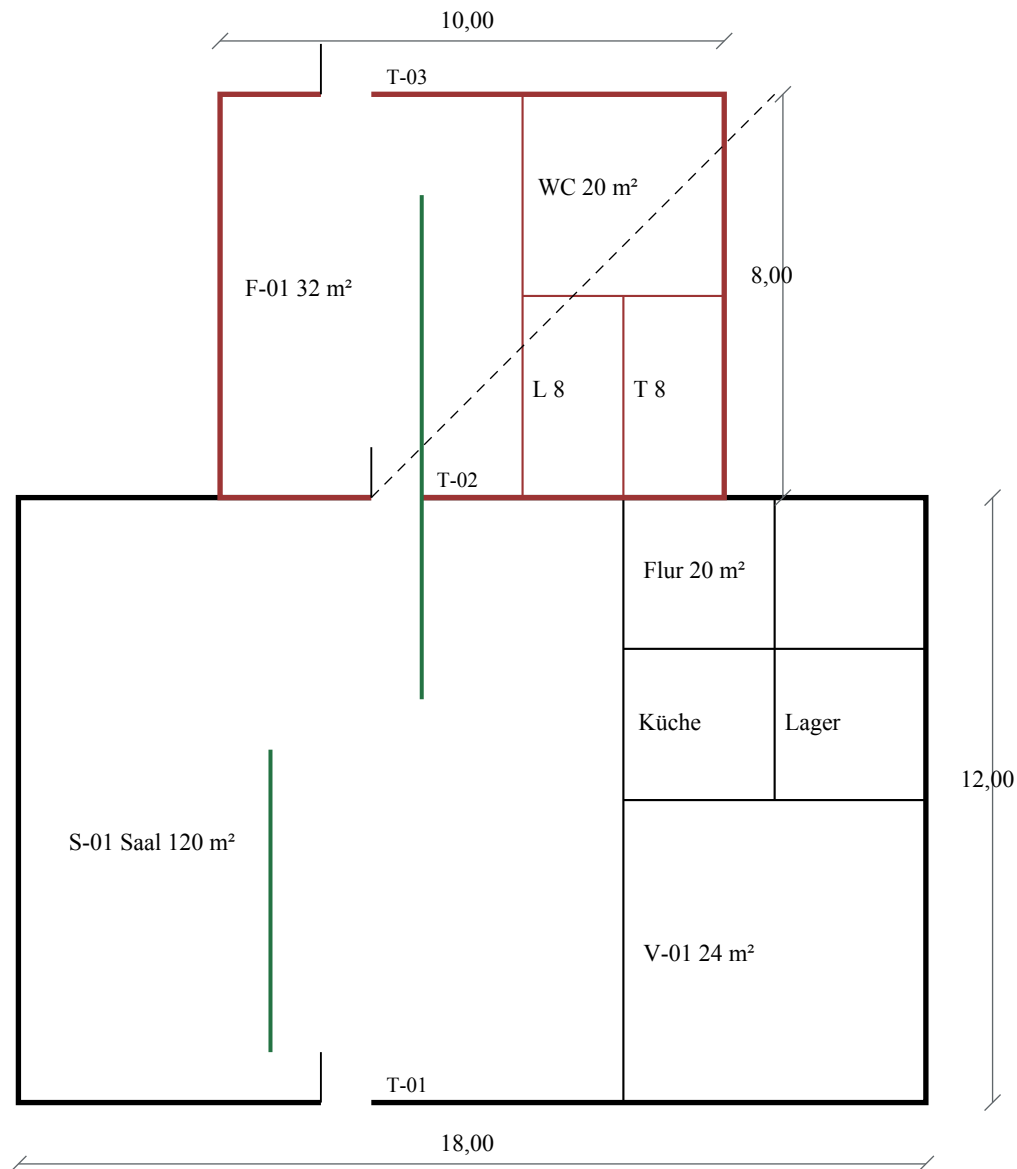

Grün: Wege zu den Ausgängen

Gestrichelt: ungeorteter Altleitungsverlauf

Fertigfußboden 112,40 m


Hof am Rampenantritt 111,80 m

Anbau: Wände 12 m², Nutzung 68 m²

Rampe nördlich des Foyers: zwei Läufe je $6,00 \times 1,50$ m, Zwischenpodest $1,50 \times 1,50$ m. Höhenunterschied 0,60 m; 5 Prozent Längsgefälle.

Wandstärken und Öffnungsrohbaumaße sind in AP-01 angegeben. Rinnen- und Sockelanschluss siehe D-12. Der Grundriss stellt keine Leitungserkundung dar.

Maßstab 1:150 bei Druck auf A4

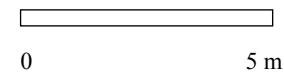

1 Erläuterungen und Zeichnungsangaben

Freigegebene Gebäudefassung Revision 00 vom 02.06.2022. Grundlage sind Genehmigung 63-2022-041, G-01 und Tragwerksplan T-02. Das Blatt legt Wandstärken, Rohbauöffnungen, Bewegungsfuge und Bezugshöhen für Los 1 fest. Maße vor Bestellung von Bauteilen örtlich prüfen. Abweichungen der Fachplanerblätter sind vor Ausführung über die Objektplanung zu klären.

Anbau außen 10,00 mal 8,00 m. Außenwand 24 cm Mauerwerk mit 16 cm Mineralwolldämmung und Putz. Bewegungsfuge zum Bestand 30 mm; keine starre Mörtelbrücke. Rohbauöffnung T-02 1,135 mal 2,135 m, T-03 1,135 mal 2,135 m. Fertige lichte Durchgangsbreite jeweils 1,00 m. Die Türanschlüsse werden am Rohbau gemeinsam aufgemessen.

Rohoberkante Bodenplatte 112,24 m, Fertigfußboden 112,40 m. Bodenaufbau 16 cm einschließlich Estrich und Belag. Fundamentbreite 50 cm, Höhe 80 cm gemäß T-02. Die Leitungsdurchführungen liegen in Hülsen und nicht im Auflagerbereich des Bestandssturzes. Die unbekannte Hofleitung ist vor Aushub zu lokalisieren; der gestrichelte Altverlauf ist kein Leitungsfreigabevermerk.

Detail D-12 regelt den Höhenanschluss. Solloberkante Rinnenrost 112,38 m, angrenzender Belag am Eingang 112,40 m. Die Oberfläche fällt zur Rinne. Das Dachgefälle ist mit 2 Prozent nach Norden vorgesehen. Vor Verfüllung sind Sockelabdichtung und Schutzlage durch die Objektüberwachung zu kontrollieren. Die Portalmarkierung einer technischen Koordinationsdatei ist keine Revision dieses freigegebenen Gebäudeplans.

Empfänger: Bürgerhaus Leinewinkel e.V.. Bezug: Bauvorhaben Lindengasse 18. Anlagen: keine. Zeichnung und Erläuterungsblatt bilden einen gemeinsamen Planstand.