


N

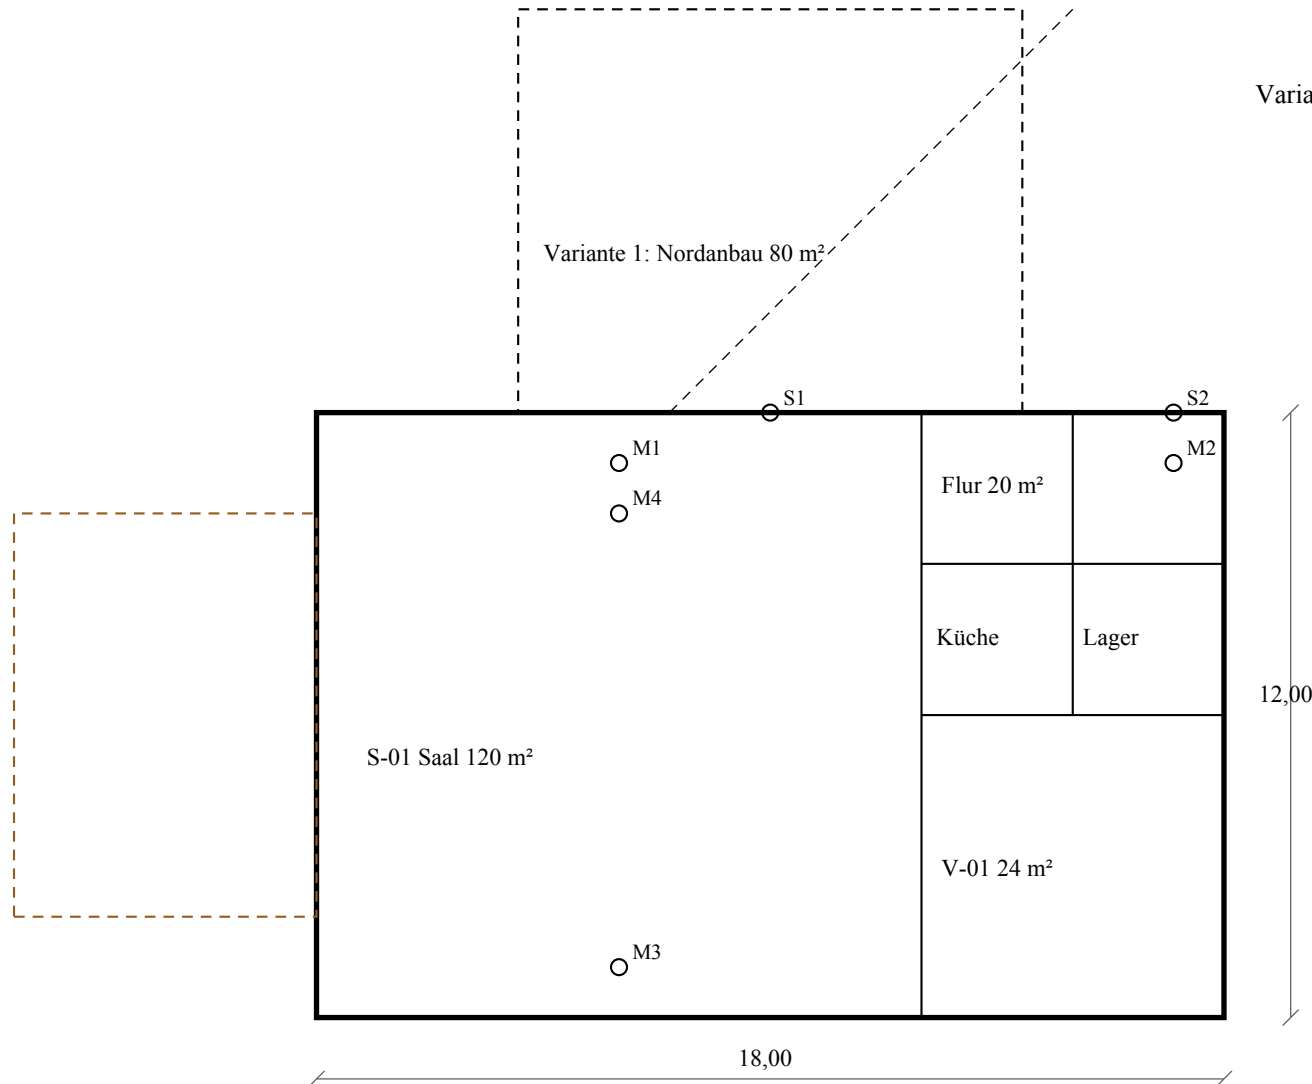

Variante 2: Westanbau 48 m²

Altleitung: nur Erinnerung des Hauswarts


Saalfußboden 112,40 m

Hof etwa 0,60 m tiefer

S1 und S2: punktuelle Suchschlitze. M1 bis M4: relative kapazitive Vergleichsanzeigen. Keine flächige Leitungssuche.

Die gestrichelten Baukörper sind untersuchte Varianten, keine Genehmigungs- oder Ausführungsplanung. Der Saalsockel ist örtlich verfärbt.

Maßstab 1:150 bei A4

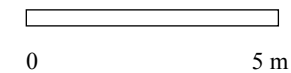

1 Erläuterungen und Zeichnungsangaben

Aufgemessen durch Lena Hartwig und Ralf Winter am 10.02.2021. Bestand außen 18,00 m mal 12,00 m, Bruttofläche 216 m². Nordpfeil und Maßketten beziehen sich auf das gesamte Bestandsgebäude. Räume: Saal 120 m², Vereinsraum 24 m², Küche 12 m², Lager 10 m² und Flur 20 m²; Wand- und Konstruktionsfläche 30 m².

Suchschlitz S1 liegt mittig an der Nordwand, S2 an der nordöstlichen Ecke. Beide wurden bis zur Fundamentoberkante geöffnet. Dort war eine Außenabdichtung nur in Resten erkennbar. Die genaue Lage einer Horizontalsperre konnte nicht festgestellt werden. Die nördliche Saalwand zeigt innen Verfärbung bis etwa 25 cm Höhe.

Kapazitive Vergleichsanzeigen: Messpunkt M1 am Saalsockel 84, M2 an der Nordostecke 79, M3 am südlichen Sockel 38 und M4 in 1,20 m Höhe an der Nordwand 35 Geräteeinheiten. Das Gerät liefert relative Vergleichswerte, keine Masseprozent. Die Aufnahmesituation war unbeheizt bei etwa 7 Grad Raumtemperatur.

Der gestrichelte Leitungsverlauf ist ausschließlich die Erinnerung des Hauswarts aus der Skizze von 1992. Er ist nicht geortet und darf nicht als gesicherte Lage für Erdarbeiten verwendet werden. Eine flächige Untersuchung des Hofes wurde nicht durchgeführt. Die Variantenfelder zeigen die Lage des möglichen Nordanbaus mit 10,00 mal 8,00 m und des alternativen Westanbaus mit 6,00 mal 8,00 m; sie sind keine Ausführungsfreigabe.

Empfänger: Bürgerhaus Leinewinkel e.V.. Bezug: Bauvorhaben Lindengasse 18. Anlagen: keine. Zeichnung und Erläuterungsblatt bilden einen gemeinsamen Planstand.