


Schnitt durch Tür T-03 und Rinne · Detail 1:10

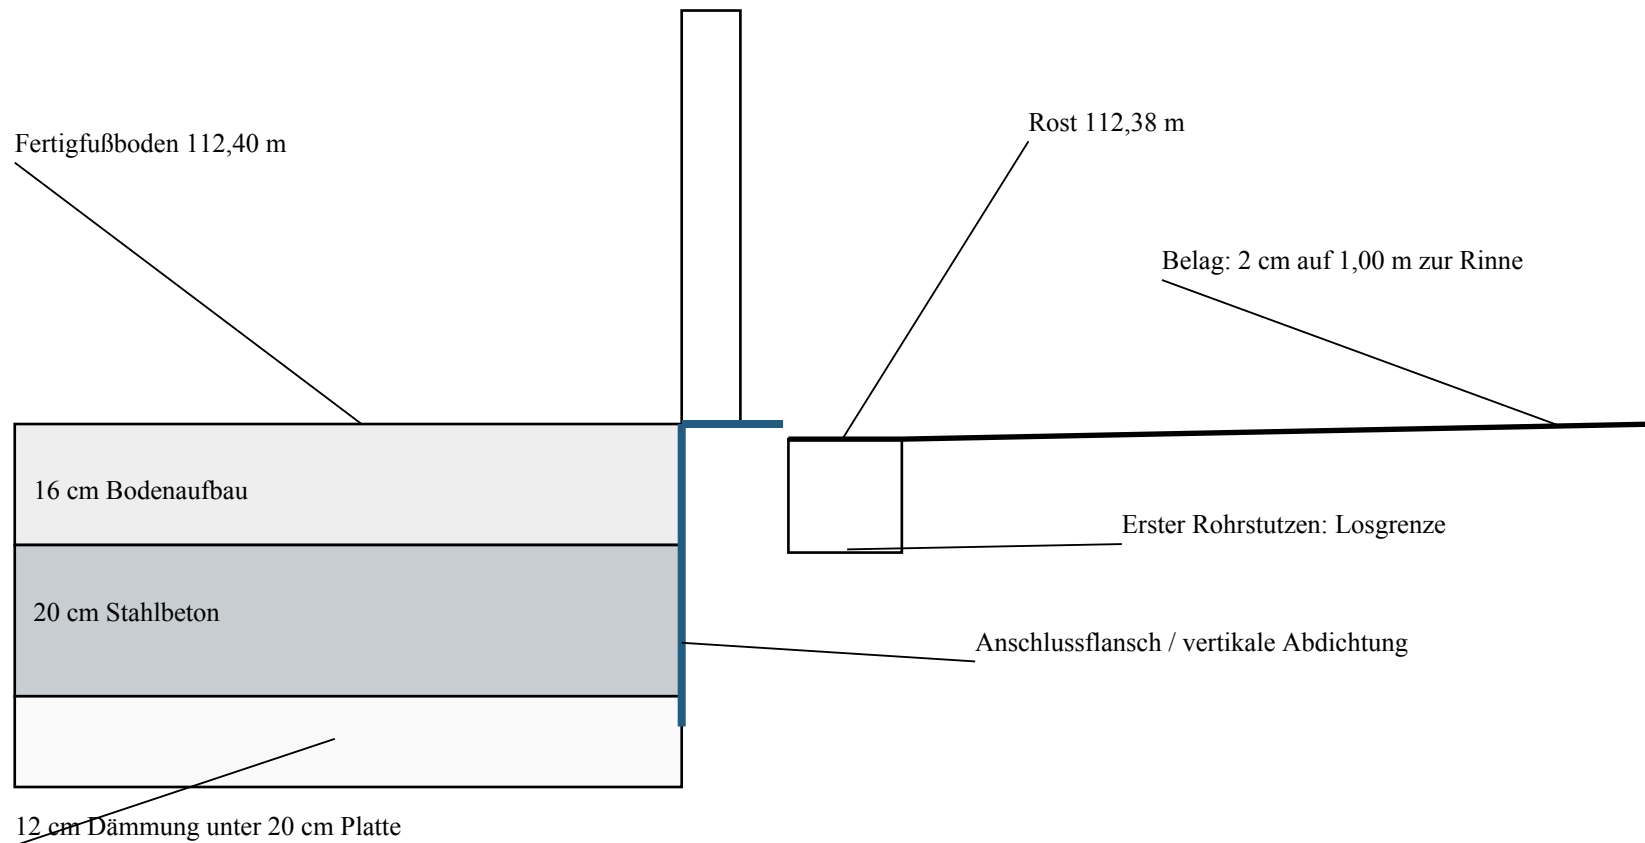

Blau: Abdichtungsführung. Höhen beziehen sich auf den örtlichen Projektbezug. Rinne 15 cm lichte Breite; Anschluss an den Türflansch vor Verdecken kontrollieren. Keine Horizontalsperre im Altbau enthalten.

1 Erläuterungen und Zeichnungsangaben

Detailblatt D-12 Revision 00, freigegeben durch Lena Hartwig am 06.06.2022. Das Detail gehört zu AP-01 und zum Leistungsverzeichnis Los 1. Es zeigt den örtlichen Eingangsanschluss im Schnitt; die Rampenlängen werden im Grundriss bestimmt. Es ist kein flächiger Sanierungsplan für den gesamten Altbau.

Der Fertigfußboden liegt bei 112,40 m. Der Rinnenrost unmittelbar vor dem Zugang erhält Sollhöhe 112,38 m. Der befestigte Anschlussbereich fällt auf einem Meter Länge um 2 cm zur Rinne. Die Türschwelle bildet keinen aufstehenden Absatz. Der Rinnenkasten ist gegen den Türanschluss abzudichten und am ersten Stutzen an die Grundstücksleitung anzuschließen.

Die zweilagige vertikale Sockelabdichtung wird auf tragfähigem gereinigtem Untergrund aufgebracht und mindestens bis 30 cm über anschließendes Gelände geführt, soweit keine Türöffnung liegt. Am niveaugleichen Türanschluss wird sie an den hierfür geeigneten Anschlussflansch geführt. Die Schutzlage darf beim Verfüllen nicht verrutschen. Der Übergang zur Bestandswand ist vor dem Verdecken fotografisch und im Bautagebuch festzuhalten.

Die Abdichtung im Sockelbereich ersetzt keine nachträgliche Horizontalsperre im Altbau. Vor Neuverputz sind die Befunde im Innenbereich aufzunehmen. Zuständig für Rinne und direkten Anschluss ist Los 1; ab dem ersten Rohrstutzen liegt die Leistung bei den Außenanlagen. Die Durchgängigkeit ist gewerkeübergreifend vor Übergabe zu prüfen. Geänderte Höhen aus Haustechnikblättern bedürfen einer ausdrücklichen Revision dieses Details.

Empfänger: Bürgerhaus Leinewinkel e.V.. Bezug: Bauvorhaben Lindengasse 18. Anlagen: keine. Zeichnung und Erläuterungsblatt bilden einen gemeinsamen Planstand.